



Projekt	Dertingen
Bearbeiter	Zeynep Yalcinkaya
Datum	06/04/2025
Blatt	Dert_01 1/2
Maßstab	1:750


Legende

- Pop
- Dp
- Manhole
- ▢ Duct_Joint
- ▲ Duct_Ende

Trench

- Bürgersteig
- Garden Trench
- Strasse
- Strassenkreuzung
- Dp_Cluster
- Dp_Cluster

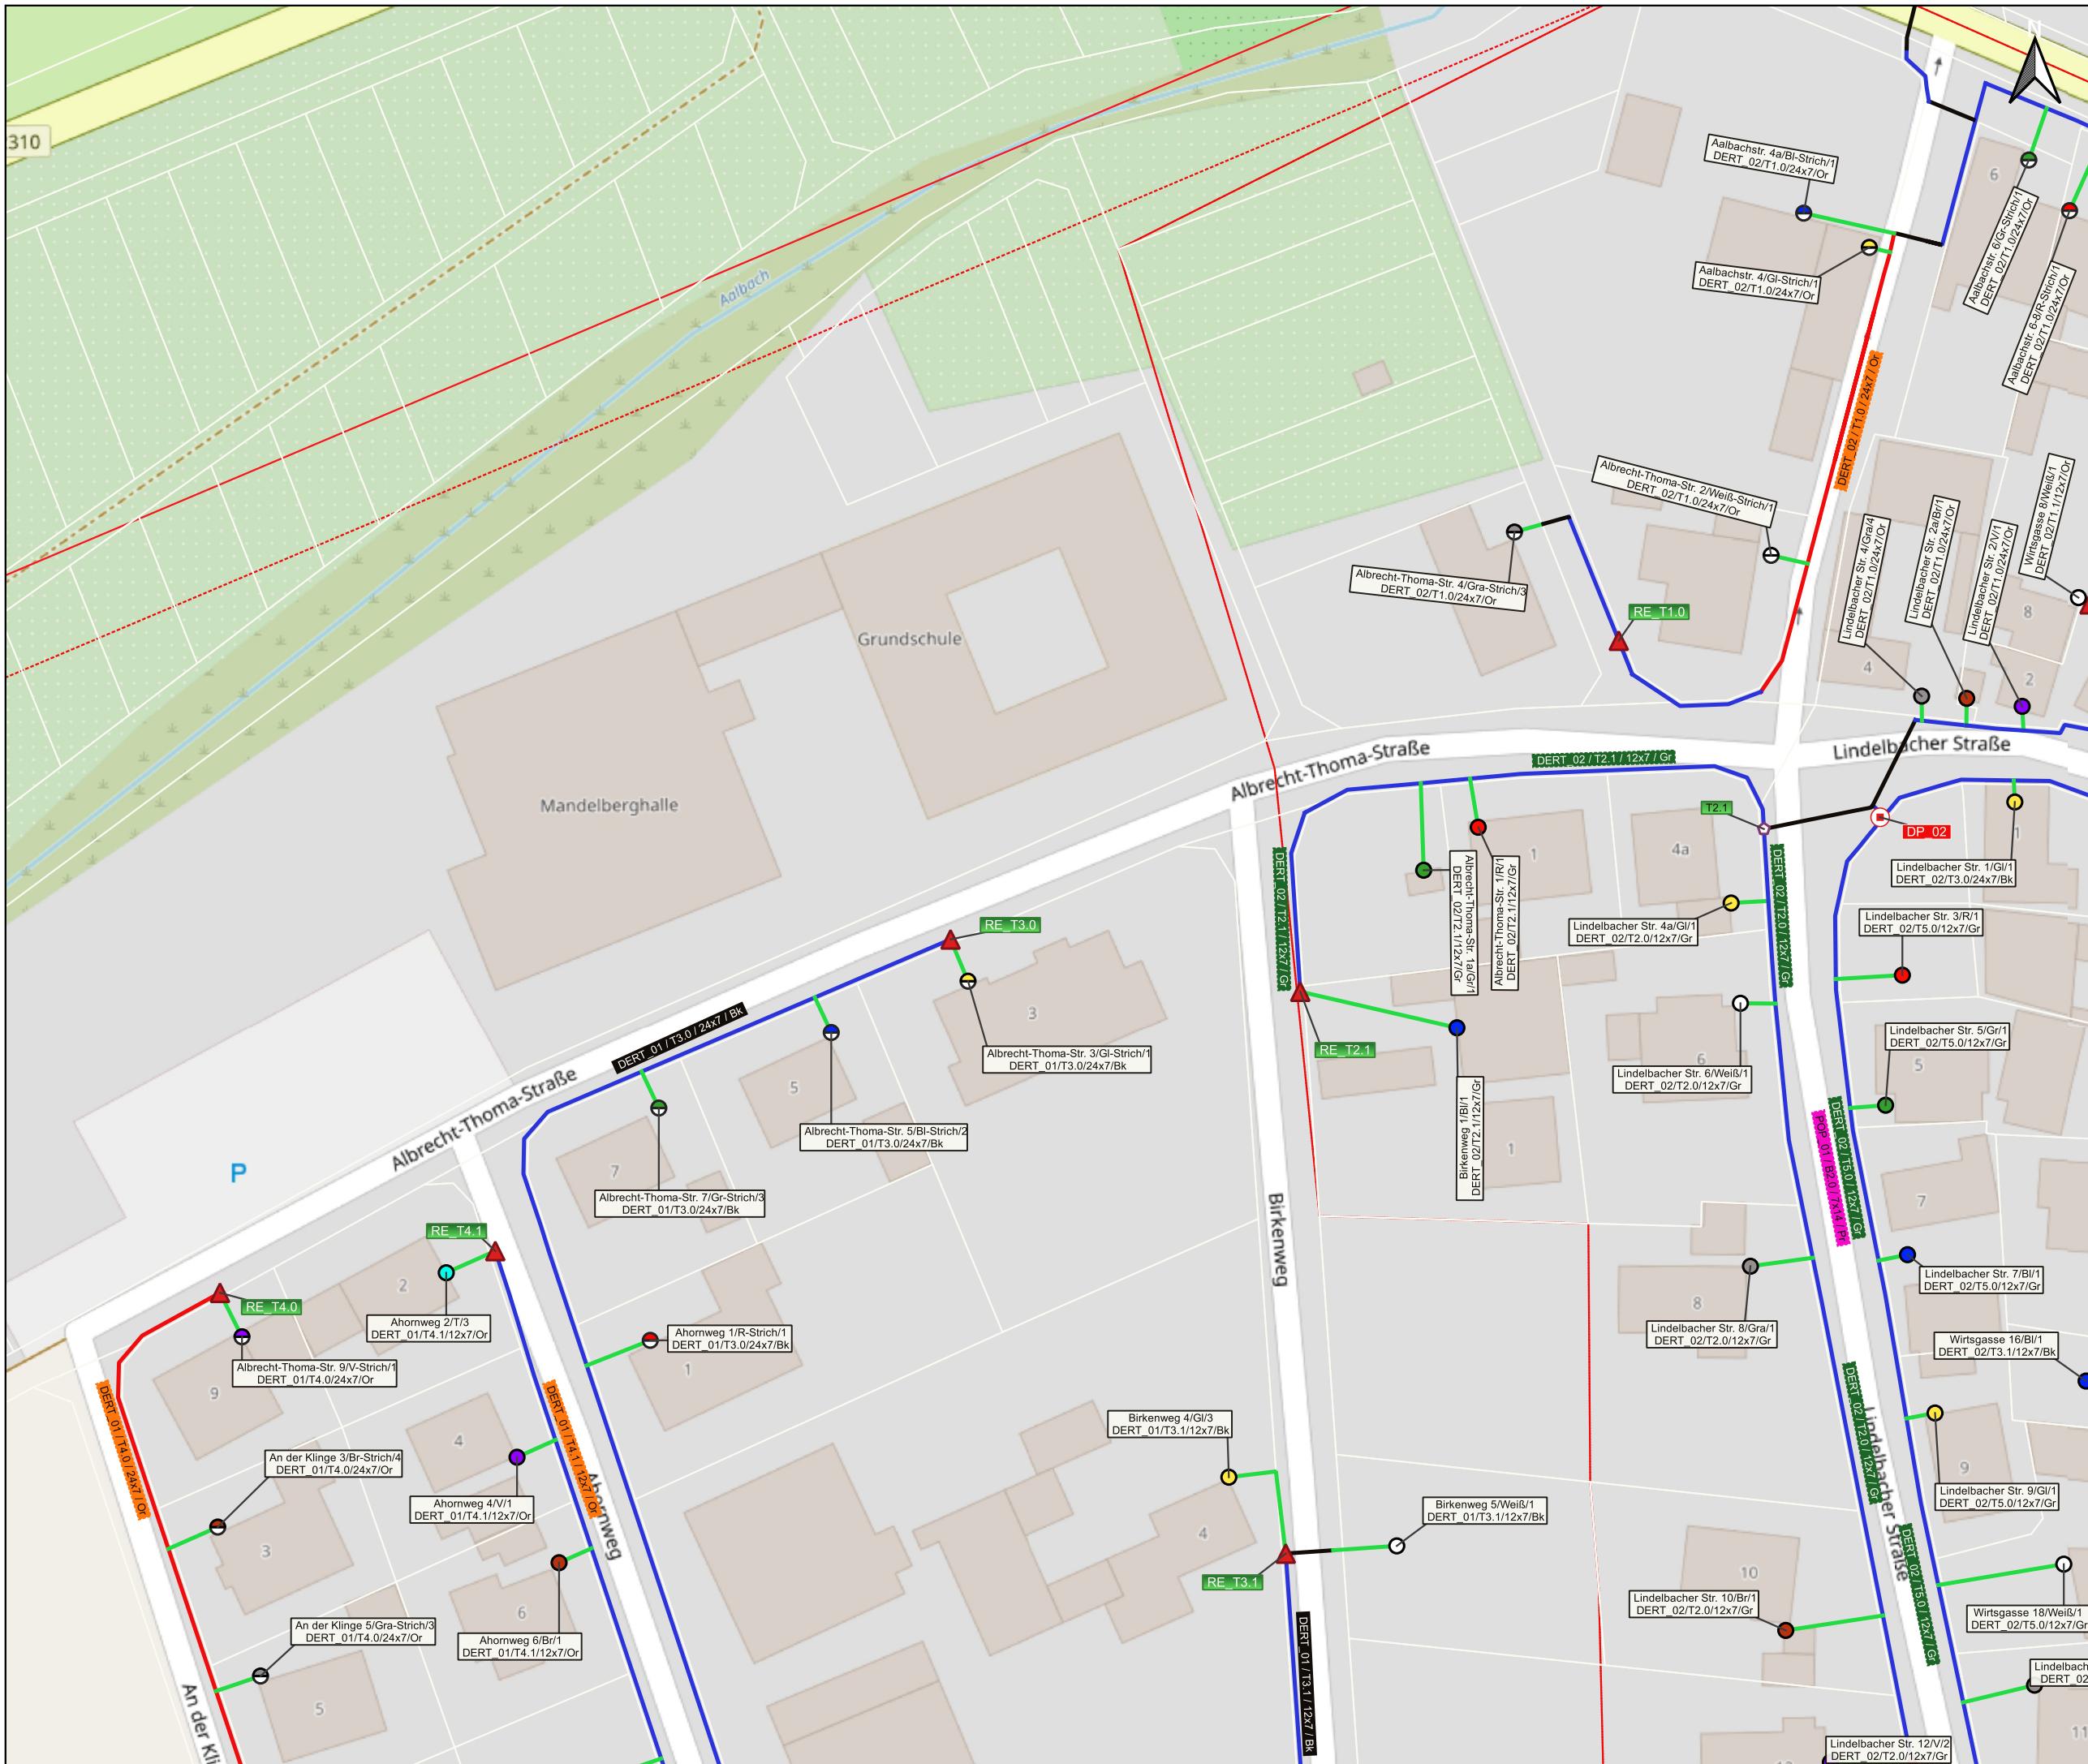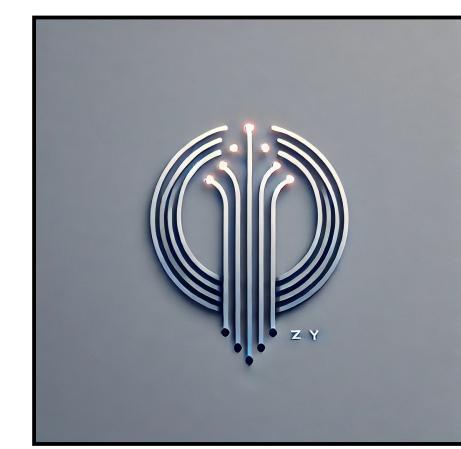

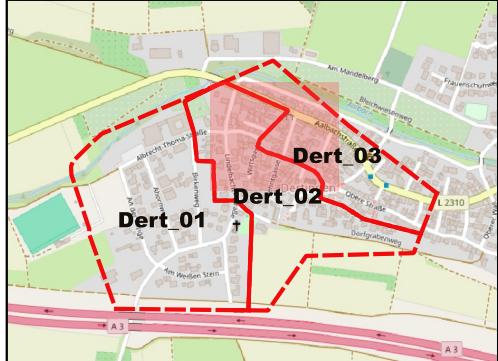	Dertingen
Projekt	Zeynep Yalcinkaya
Bearbeiter	06/04/2025
Datum	Dert_03 1/2
Blatt	1:750

Legende

- Pop
- Dp
- Manhole
- Duct_Joint
- Duct_Ende

Trench

- Bürgersteig
- Garden Trench
- Strasse
- Strassenkreuzung
- Dp_Cluster
- Dp_Cluster





Projekt	Dertingen
Bearbeiter	Zeynep Yalcinkaya
Datum	06/04/2025
Blatt	Dert_03 2/2
Maßstab	1:750


Legende

- Hexagon with blue border: Pop
 - Square with red border: Dp
 - Square with orange border: Manhole
 - Pentagon with purple border: Duct_Joint
 - Triangle with red border: Duct_Ende

Trench

- Bürgersteig
 - Garden Trench
 - Strasse
 - Strassenkreuzung
 - Dp_Cluster
 - Dp Cluster

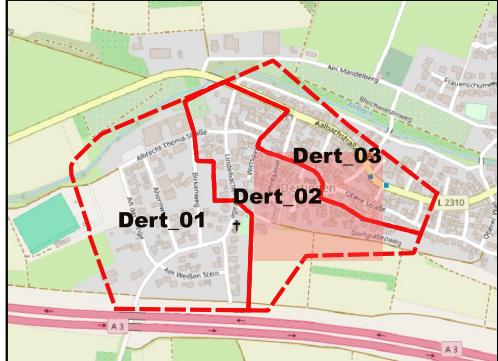


	Dertingen
Projekt	Dertingen
Bearbeiter	Zeynep Yalcinkaya
Datum	06/04/2025
Blatt	Dert_02 2/2
Maßstab	1:750

Legende

- Pop
- Dp
- Manhole
- Duct_Joint
- Duct_Ende

Trench

- Bürgersteig
- Garden Trench
- Strasse
- Strassenkreuzung
- Dp_Cluster
- Dp_Cluster

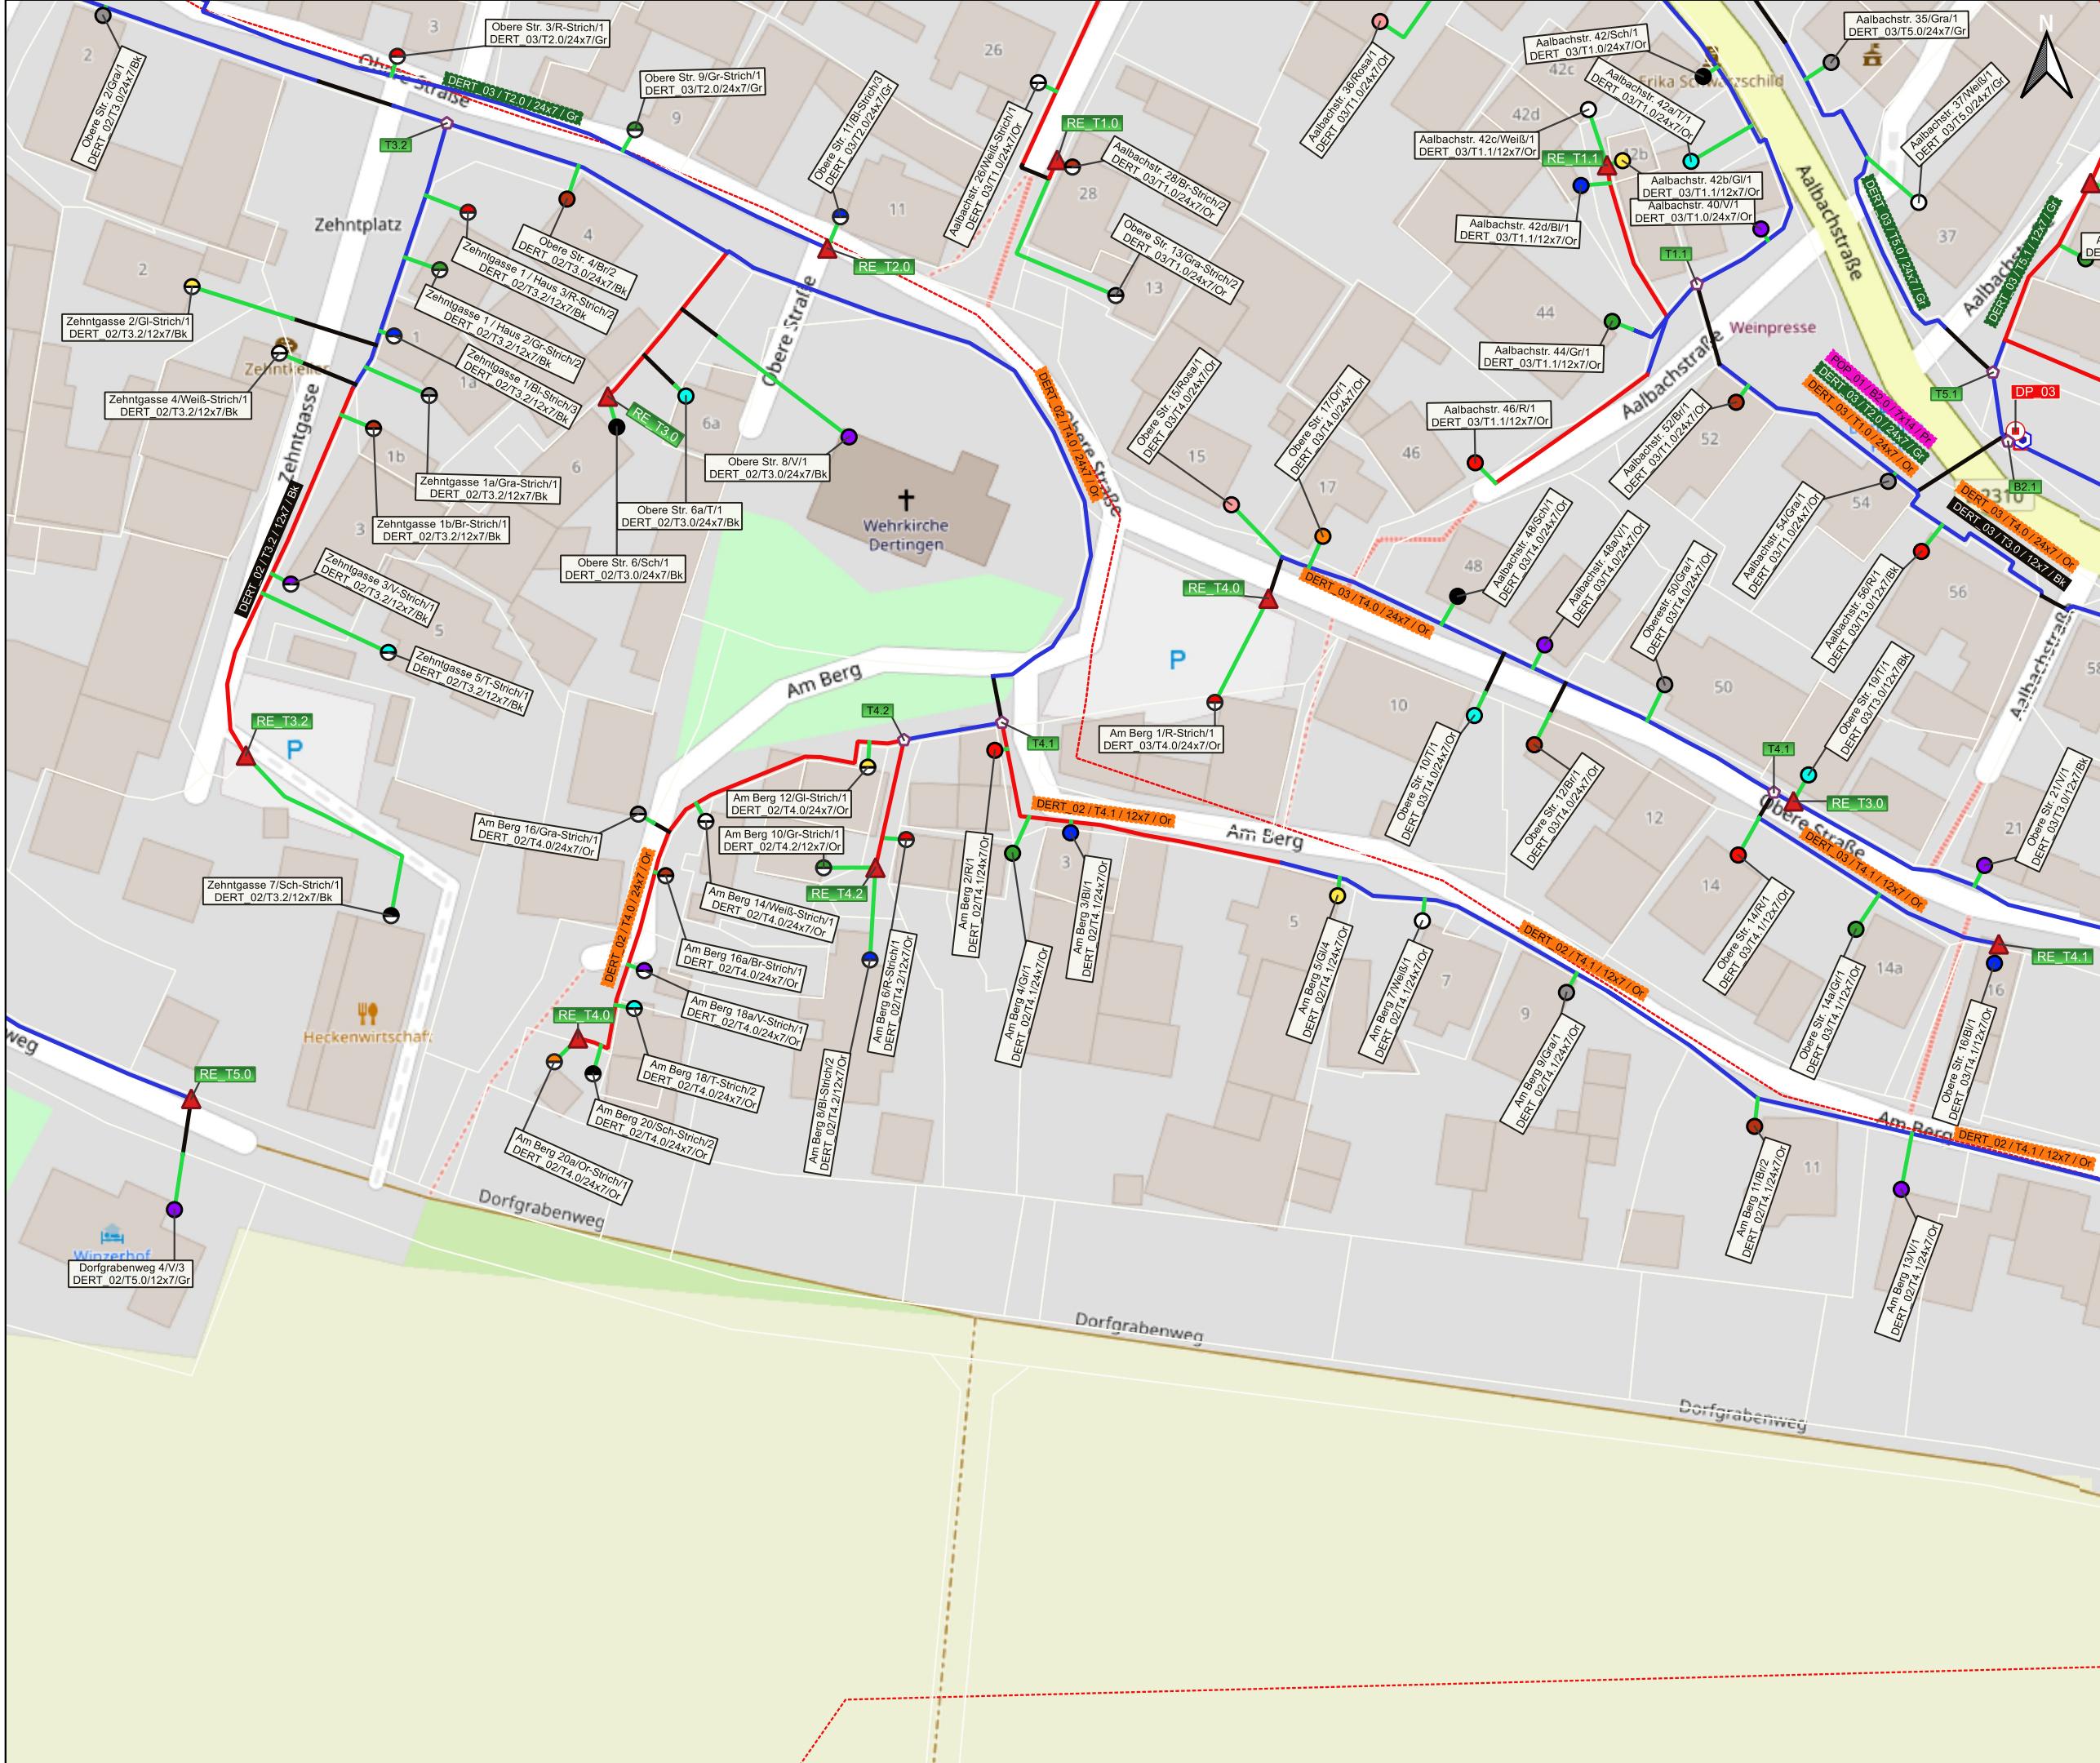


Dert_01	Dert_02
Dertingen	
Bearbeiter	Zeynep Yalcinkaya
Datum	06/04/2025
Blatt	Dert_02 1/2
Maßstab	1:750

Legende

- Pop
- Dp
- Manhole
- ▢ Duct_Joint
- ▲ Duct_Ende

Trench

- Bürgersteig
- Garden Trench
- Strasse
- Strassenkreuzung
- Dp_Cluster
- Dp_Cluster

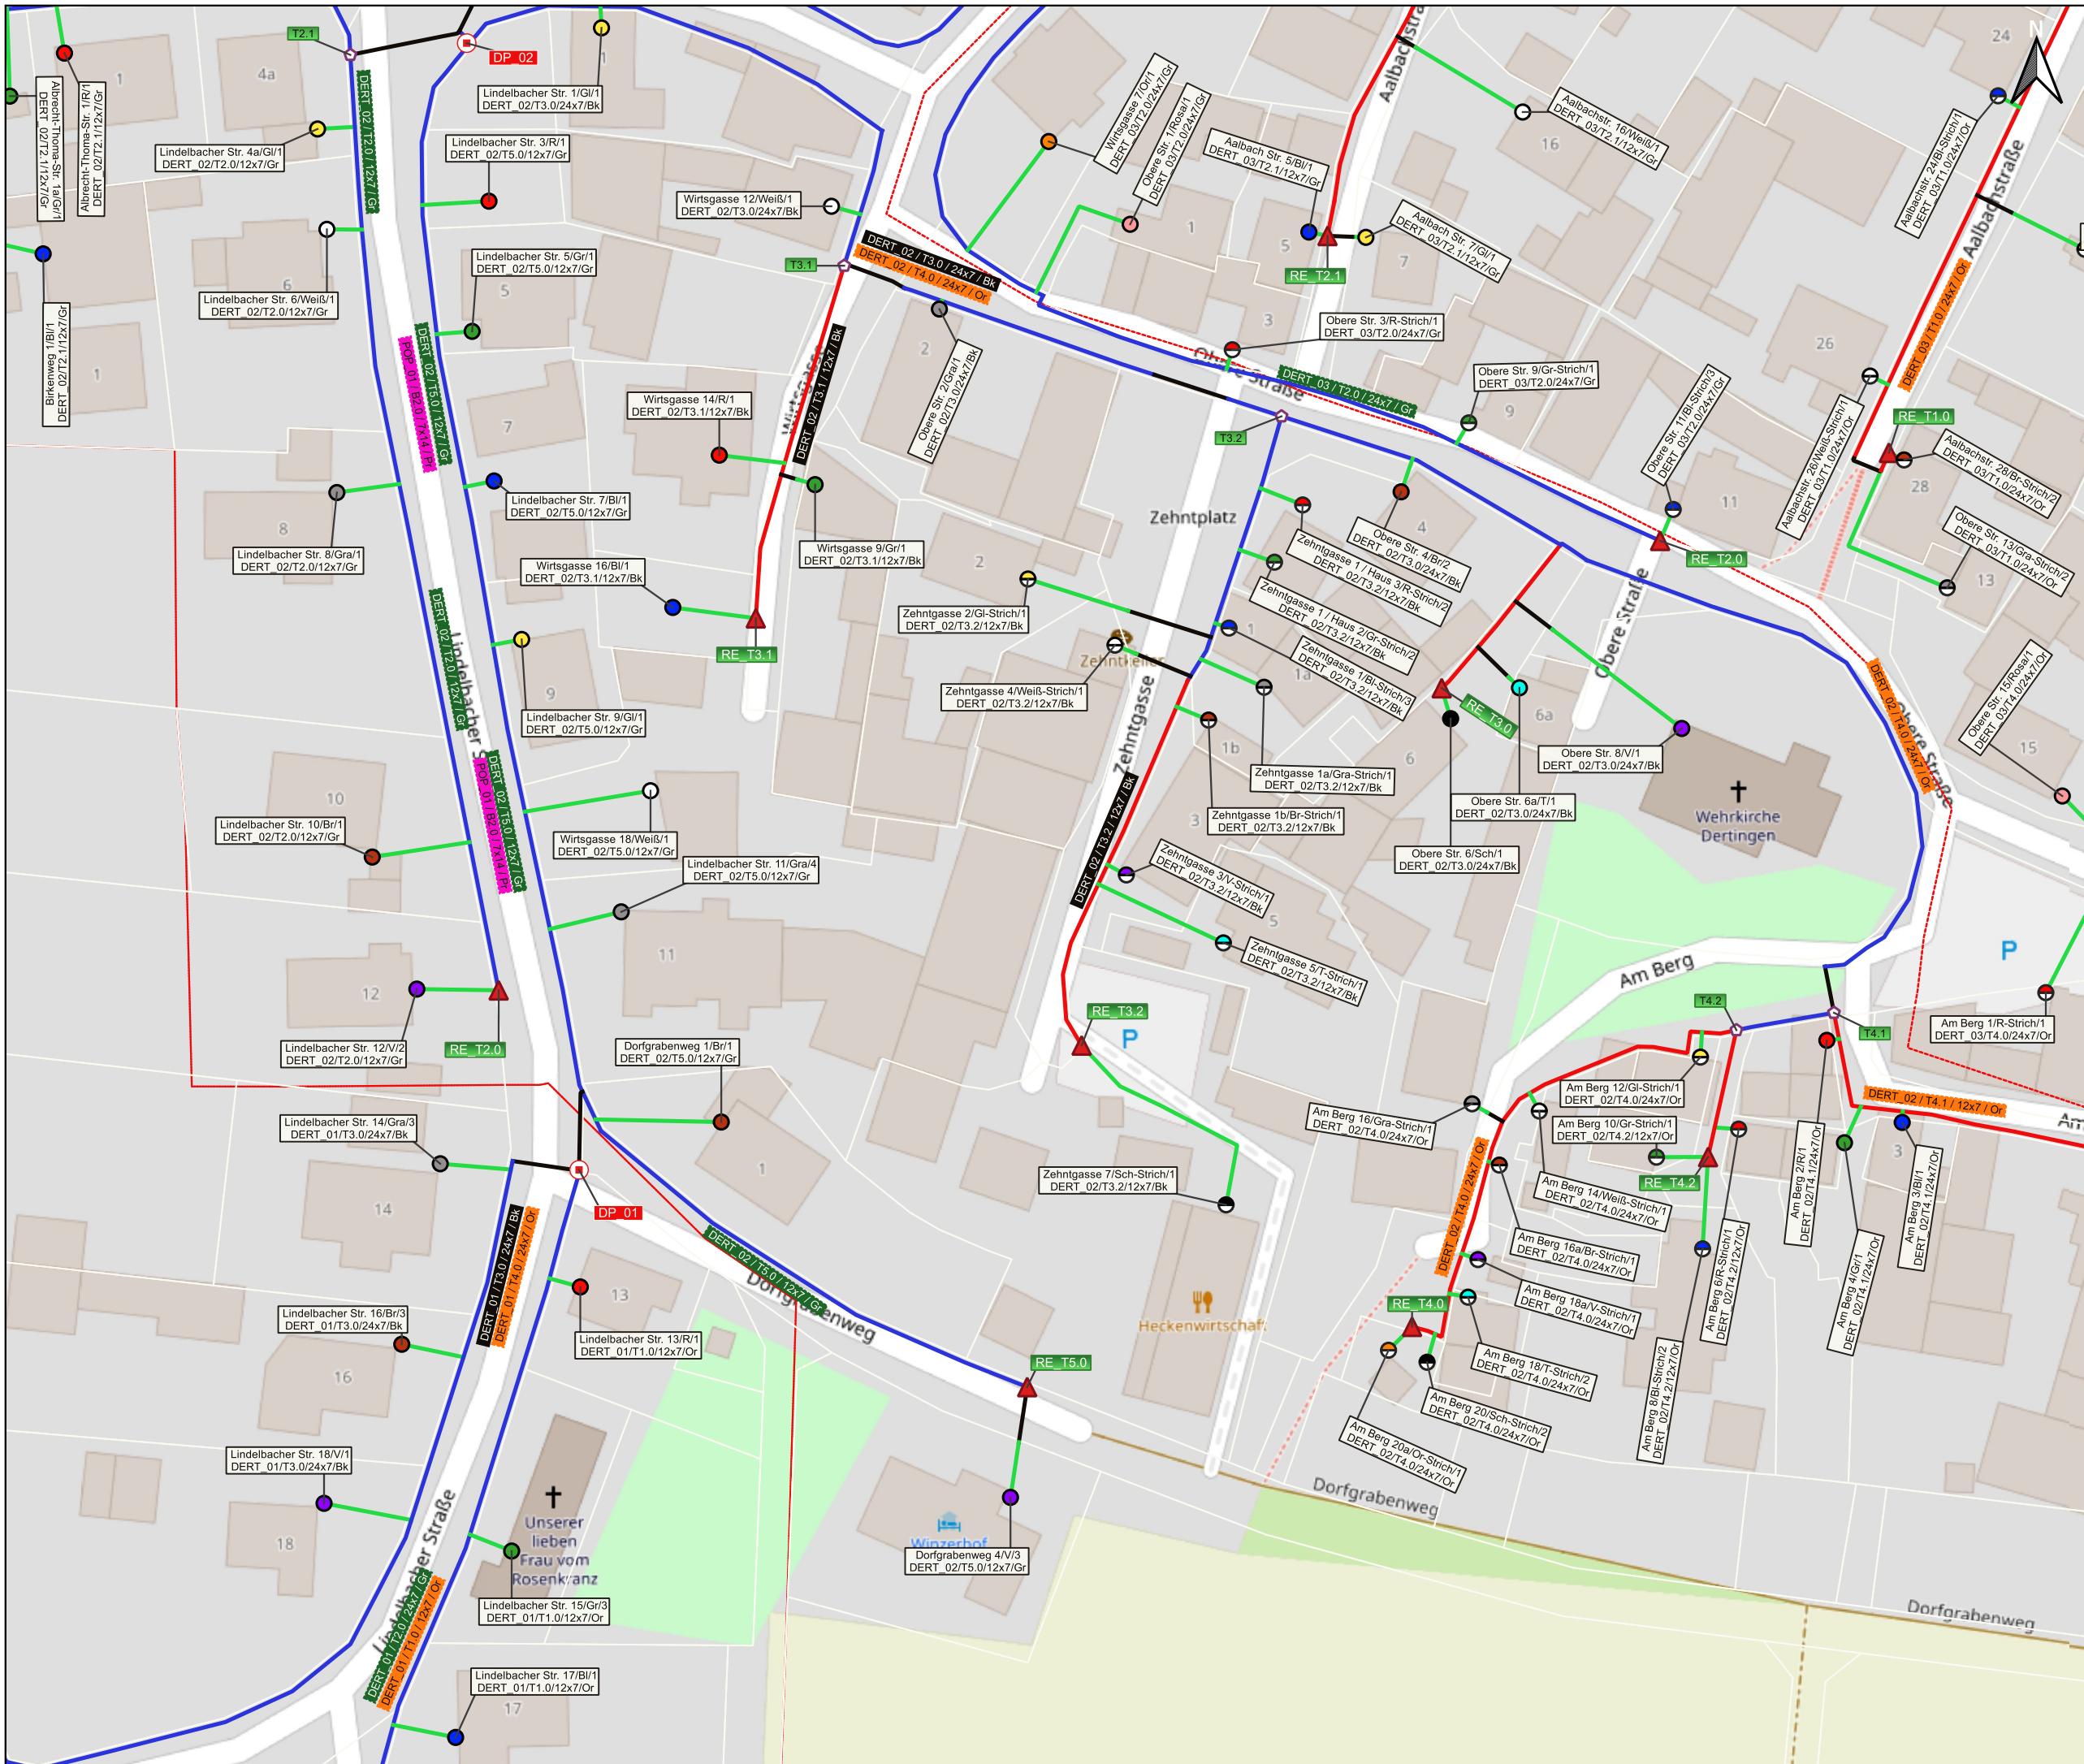

Dertingen

Projekt	Dertingen
Bearbeiter	Zeynep Yalcinkaya
Datum	06/04/2025
Blatt	DERT_01 2/2
Maßstab	1:750

Legende

- Pop
- Dp
- Manhole
- ▢ Duct_Joint
- ▲ Duct_Ende

Trench

- Bürgersteig
- Garden Trench
- Strasse
- Strassenkreuzung
- Dp_Cluster
- Dp_Cluster

